20070309900001

220/155

3/8/2007

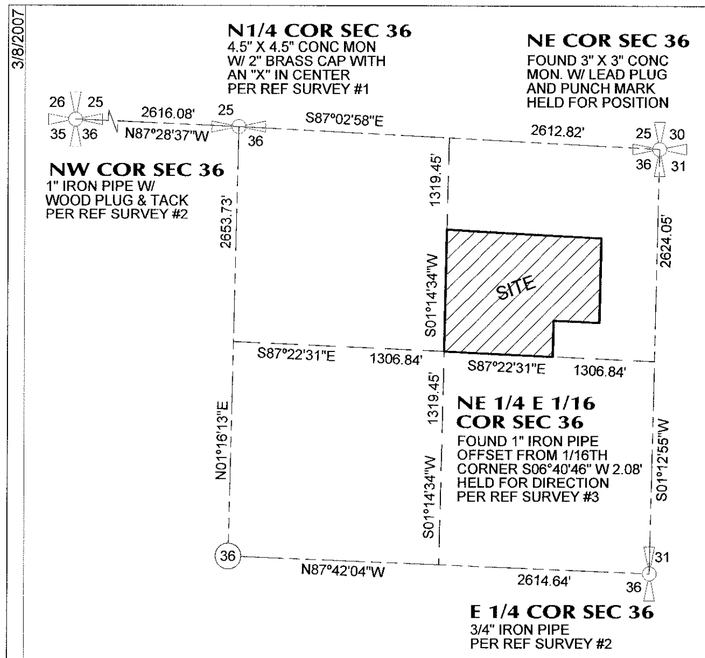

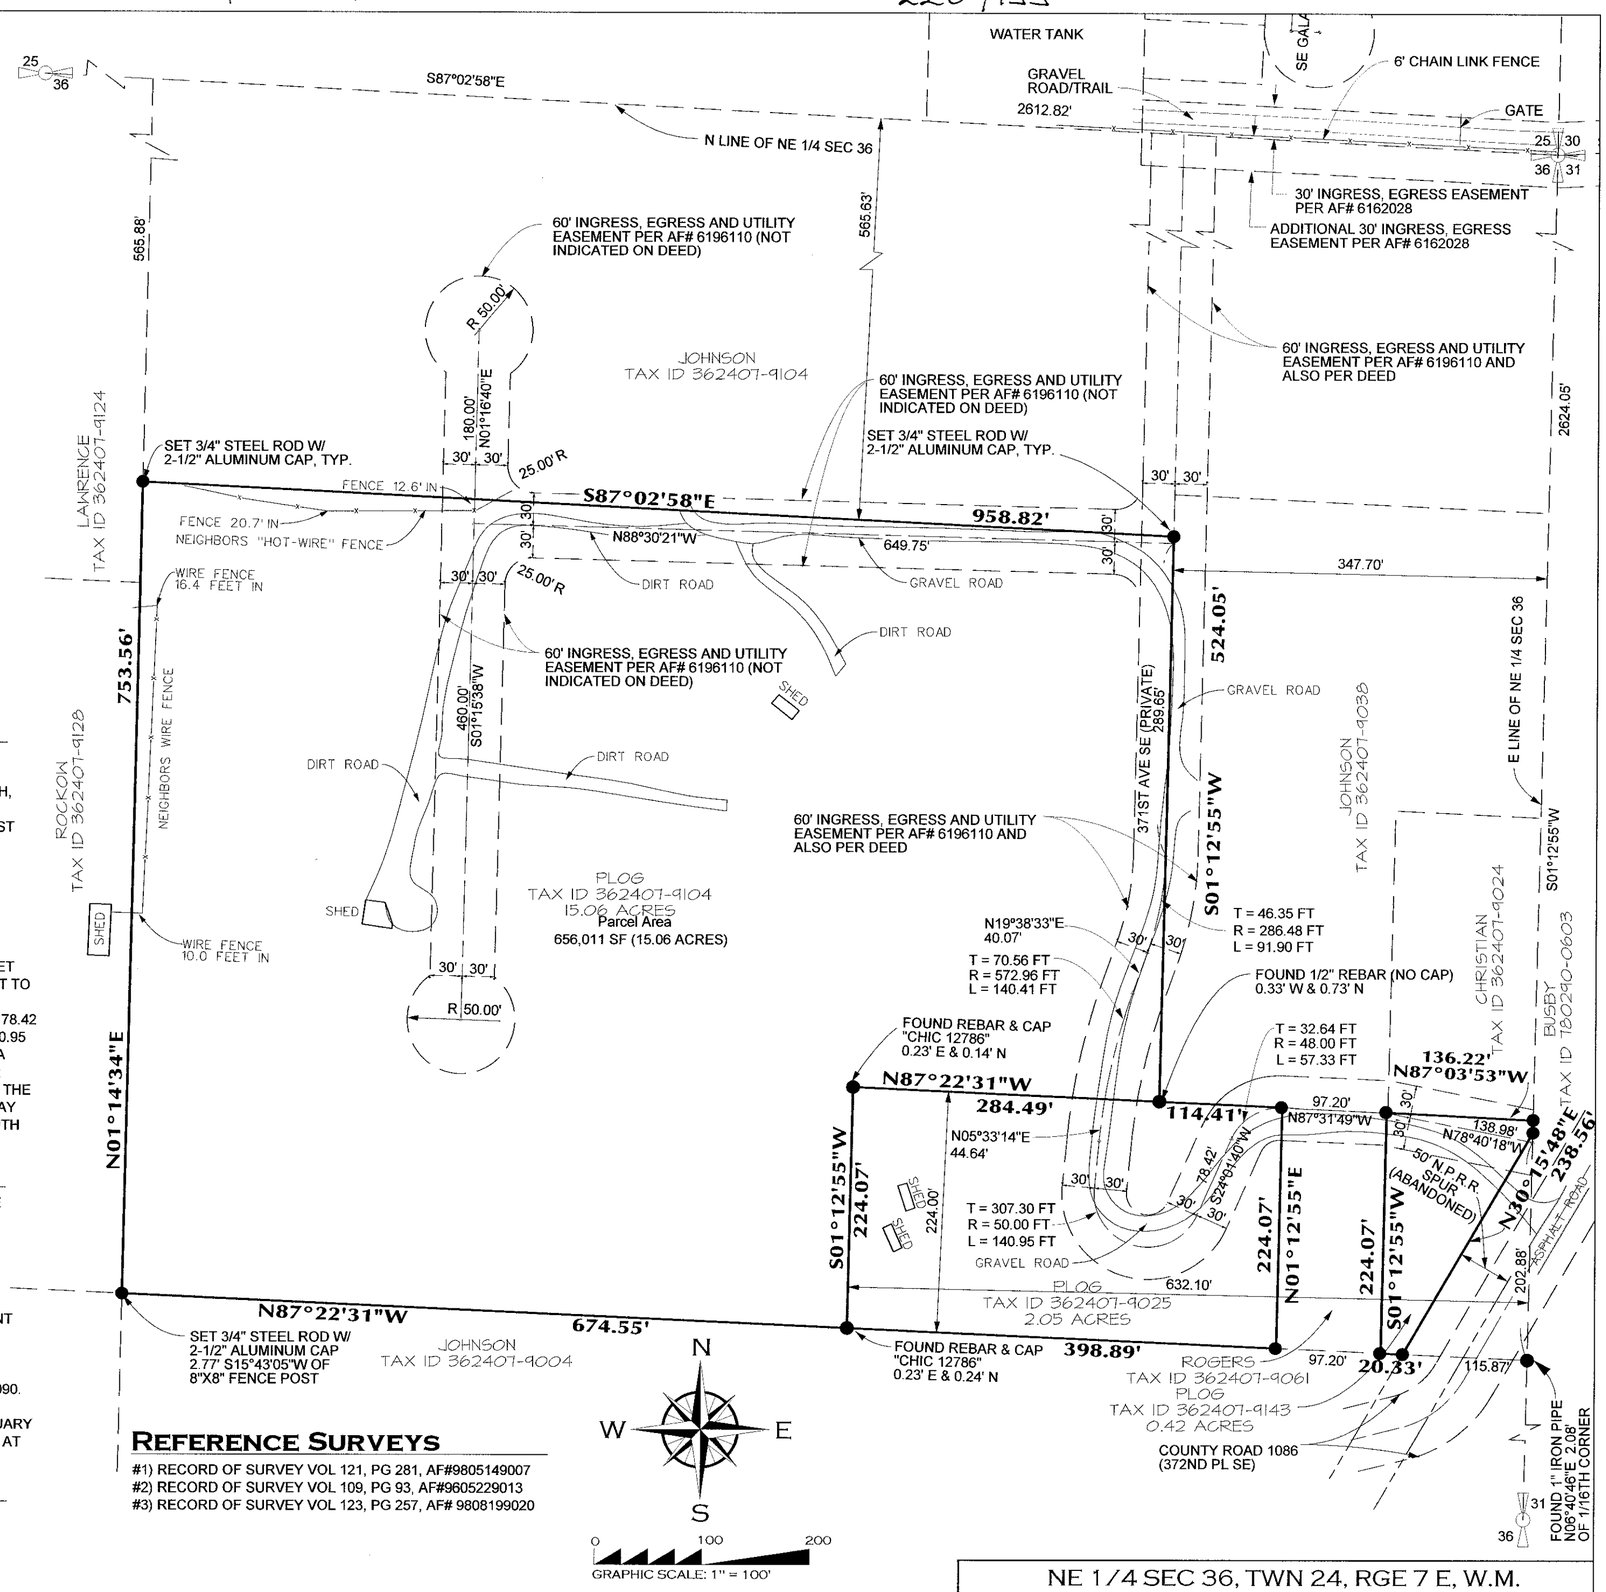

Legal Description (FROM TITLE REPORT)

PARCEL A (LAND):

THE NORTHEAST QUARTER OF THE NORTHEAST QUARTER OF SECTION 36, TOWNSHIP 24 NORTH, RANGE 7 EAST, W.M., IN KING COUNTY, WASHINGTON; EXCEPT THE NORTH 565.63 FEET LYING WEST OF THE EAST 347.7 FEET OF SAID SUBDIVISION; EXCEPT THE SOUTH 224 FEET OF THE EAST 632.1 FEET; AND EXCEPT THE EAST 347.7 FEET OF THE NORTH 1081.8 FEET.

PARCEL B (EASEMENT):

A NON-EXCLUSIVE EASEMENT FOR INGRESS AND EGRESS OVER A STRIP OF LAND 60 FEET IN WIDTH HAVING 30 FEET OF SUCH WIDTH ON EACH SIDE OF THE FOLLOWING DESCRIBED CENTERLINE: BEGINNING AT A POINT ON EAST LINE SAID SECTION 36, TOWNSHIP 24 NORTH, RANGE 7 EAST, W.M., IN KING COUNTY, WASHINGTON, WHICH IS NORTH 1^22 33" EAST 202.88 FEET FROM THE NORTH 1/16 CORNER OF SAID EAST LINE; THENCE NORTH 78^30 40" WEST 138.98 FEET TO AN ANGLE POINT; THENCE NORTH 87^22 11" WEST 97.55 FEET; THENCE ALONG A CURVE TO THE LEFT WITH A RADIUS OF 48.00 FEET A DISTANCE OF 57.33 FEET; THENCE SOUTH 24^11 18" WEST 78.42 FEET; THENCE ALONG A CURVE TO THE RIGHT WITH A RADIUS OF 50.00 FEET A DISTANCE OF 140.95 FEET; THENCE NORTH 5^42 52" EAST 44.64 FEET; THENCE ALONG A CURVE TO THE RIGHT WITH A RADIUS OF 572.96 FEET A DISTANCE OF 140.41 FEET; THENCE NORTH 19^48 11" EAST 40.07 FEET; THENCE ALONG A CURVE TO THE LEFT WITH RADIUS OF 286.48 FEET A DISTANCE OF 91.90 FEET THE NORTH 1^22 33" EAST 289.65 FEET TO AND INTERSECTION WITH CENTERLINE ROAD RIGHT OF WAY TO THE WEST: THENCE CONTINUING NORTH 1^22 33" EAST 565.63 FEET TO AN INTERSECTION WITH THE NORTH LINE OF SAID SECTION 36, IN KING COUNTY, WASHINGTON.

Basis of Bearings

RECORD OF SURVEY, AS RECORDED IN VOLUME 121 OF SURVEYS ON PAGE 281 AND IN VOLUME 109 OF SURVEYS ON PAGE 93, RECORDS OF KING COUNTY, WASHINGTON.

ACCEPTED THE SECTION BREAKDOWN BASED ON VARIOUS FOUND MONUMENTS.

General Notes

1. THIS SURVEY IS BASED ON THE FIRST AMERICAN TITLE INSURANCE COMPANY COMMITMENT FOR TITLE INSURANCE, ORDER NO. 4268-632282, DATED MARCH 3, 2006 AT 7:30 A.M.
2. INSTRUMENTATION FOR THIS SURVEY WAS A 3-SECOND NIKON DTM 521 TOTAL STATION. PROCEDURES USED IN THIS SURVEY MEET OR EXCEED STANDARDS SET BY WAC 332-130-090.
3. THE INFORMATION ON THIS MAP REPRESENTS THE RESULTS OF A SURVEY MADE IN FEBRUARY 2006 AND CAN ONLY BE CONSIDERED AS INDICATING THE GENERAL CONDITIONS EXISTING AT THAT TIME.

Easements From Title Report

ITEM #5 - INGRESS, EGRESS & UTILITIES, AF# 6196110 (SHOWN ON FACE OF SURVEY)

Reference Surveys

#1) RECORD OF SURVEY VOL 121, PG 281, AF#9805149007
#2) RECORD OF SURVEY VOL 109, PG 93, AF#9605229013
#3) RECORD OF SURVEY VOL 123, PG 257, AF# 9808199020

C:\Documents and Settings\Mark Plog\Plog Ranch\Snoqualmie\PLOG-ROS.dgn

NE 1/4 SEC 36, TWN 24, RGE 7 E, W.M.

RECORDER'S CERTIFICATE

FILED FOR RECORD THIS 09 DAY OF March, 2007 AT 9:21 A.M. IN BOOK 220 OF SURVEYS PAGE 155 AT THE REQUEST OF GEODATUM, INC.

MGR. SUPT. OF RECORDS

SURVEYOR'S CERTIFICATE

THIS MAP CORRECTLY REPRESENTS A SURVEY MADE BY ME OR UNDER MY DIRECTION IN CONFORMANCE WITH THE REQUIREMENTS OF THE SURVEY RECORDING ACT AT THE REQUEST OF MARK & RHEANELL PLOG IN MARCH, 2006 & MARCH 2007

CERTIFICATE NO.: 38964

THOMAS N. WOLDENDORP — STATE OF WASHINGTON — 38964 — REGISTERED PROFESSIONAL LAND SURVEYOR — EXPIRES 7/10/2007 3/7/07

RECORD OF SURVEY FOR

MARK & RHEANELL PLOG

8215 - 371ST AVE SE
Snoqualmie, WA

© 2006, GEODATUM, INC., ALL RIGHTS RESERVED

www.geodatum.com
GeoDatum Inc
SURVEY-CIVIL-STRUCTURAL
1505 NW Mall Street
Issaquah, WA 98027
(425) 837-8083

SHEET: 1
OF: 1